


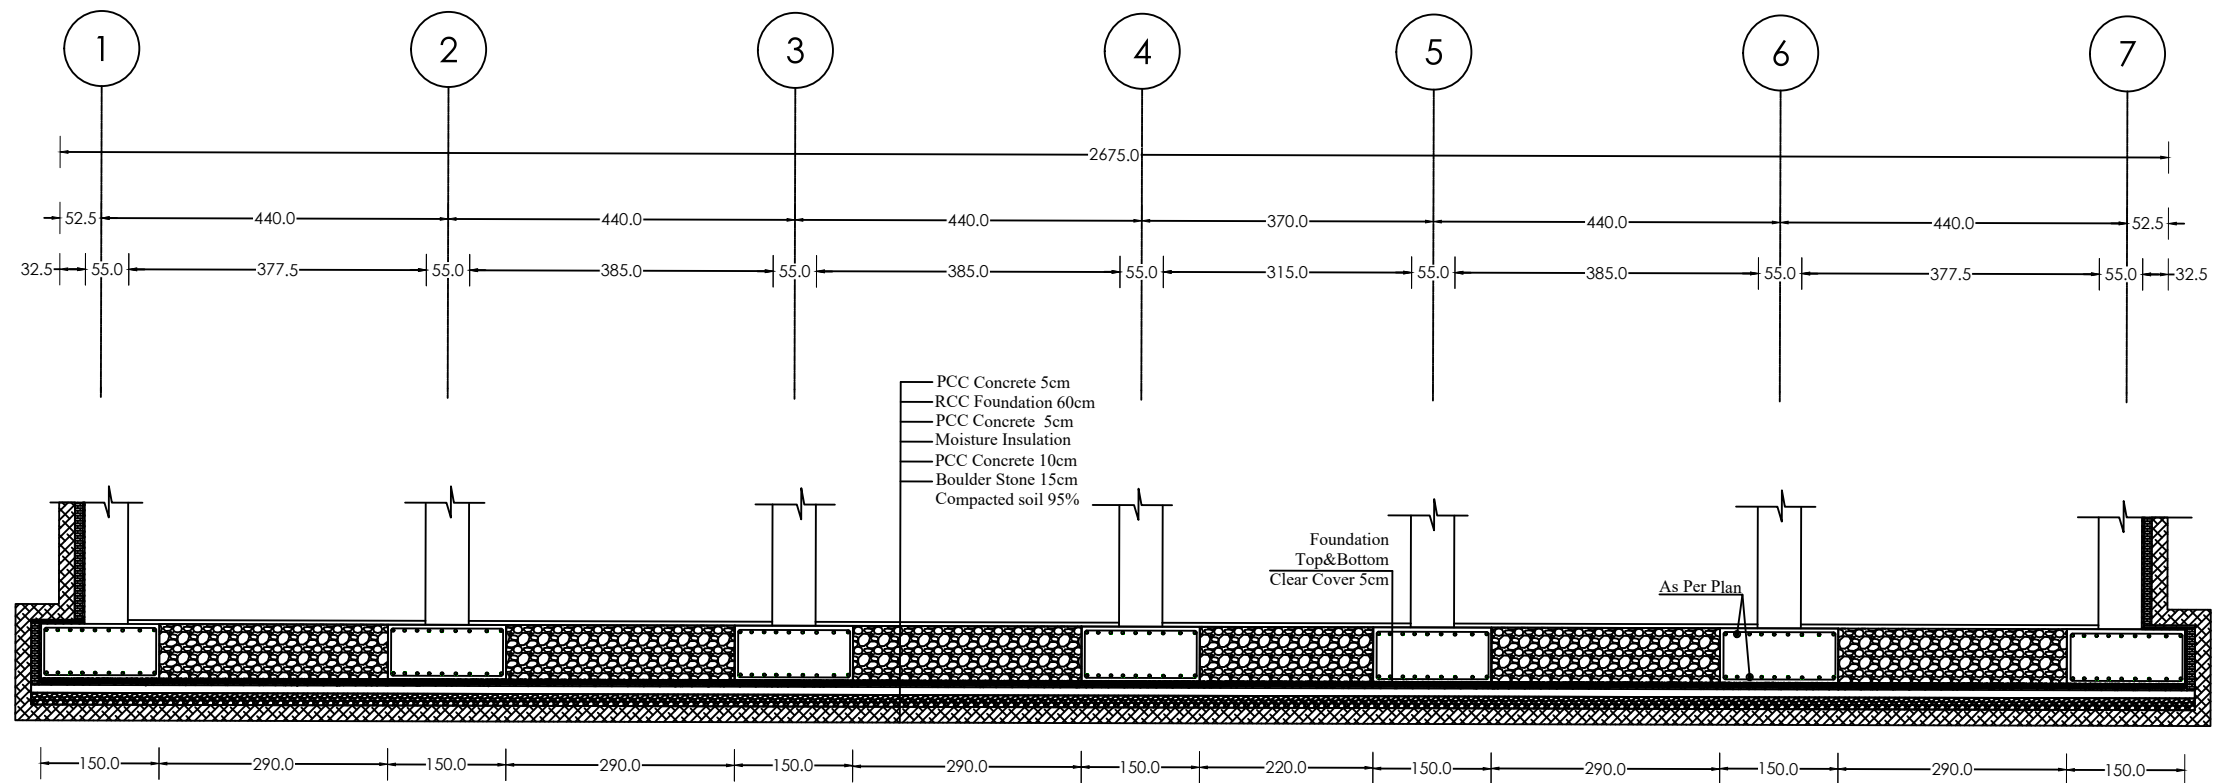

09 | Section A-A FOUNDATION
S-09 | REF. | SCALE: 1:100

NOTES:
1-FOUNDATION DEPTH =70cm
2-Fc = 4000 psi
3-Fy = 60000 psi