


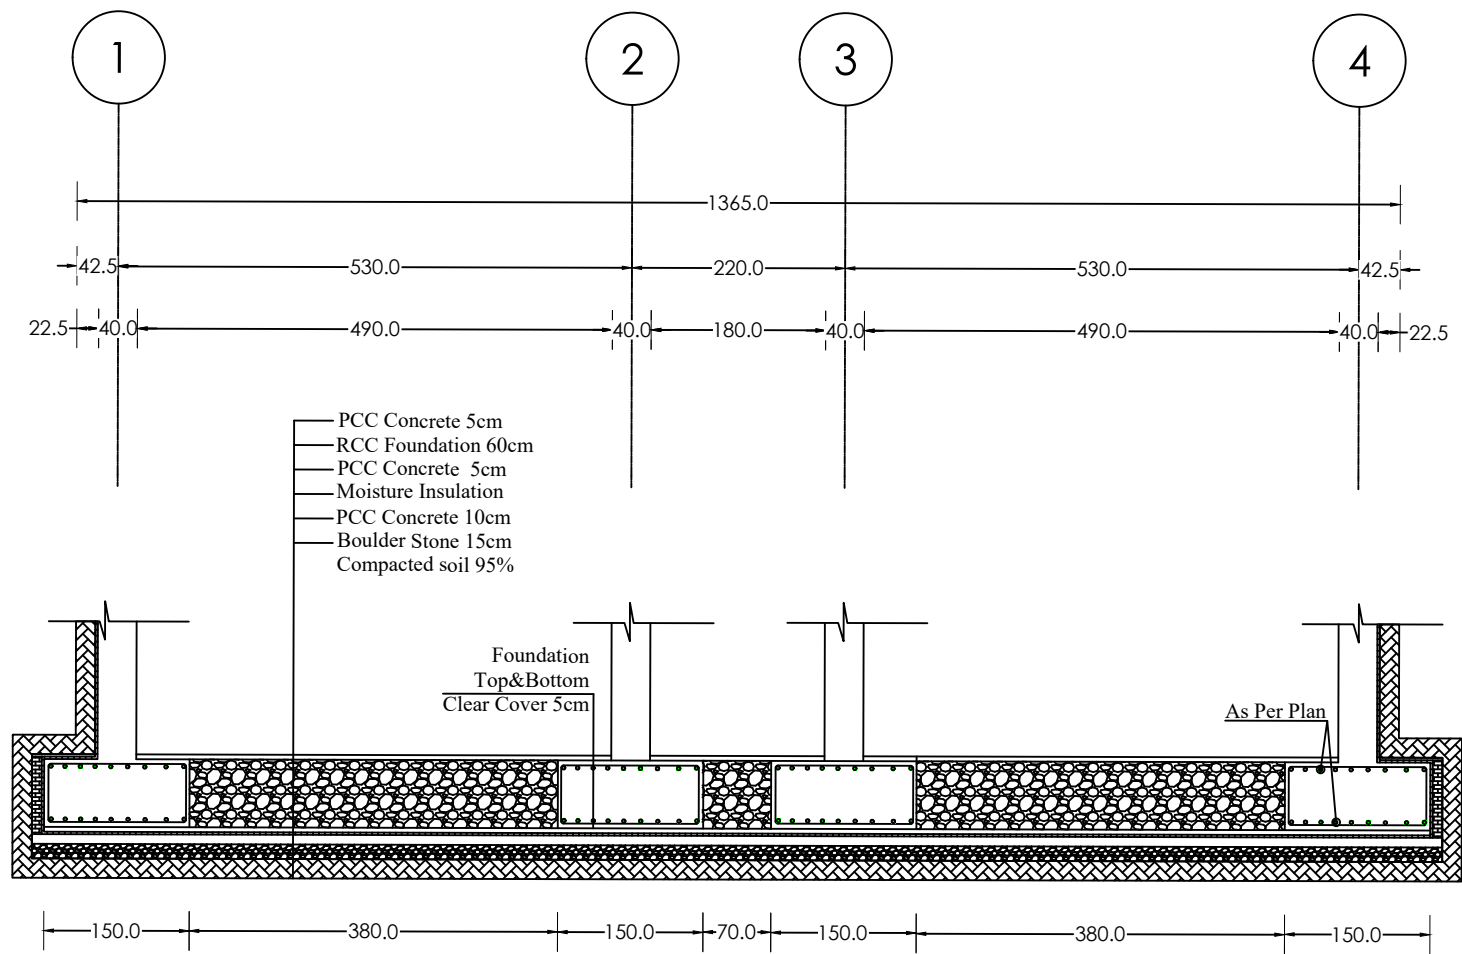

09 | Section B-B FOUNDATION
 S-09 | REF. | SCALE: 1:100

NOTES:
 1-FOUNDATION DEPTH =70cm
 2-Fc = 4000 psi
 3-Fy = 60000 psi