


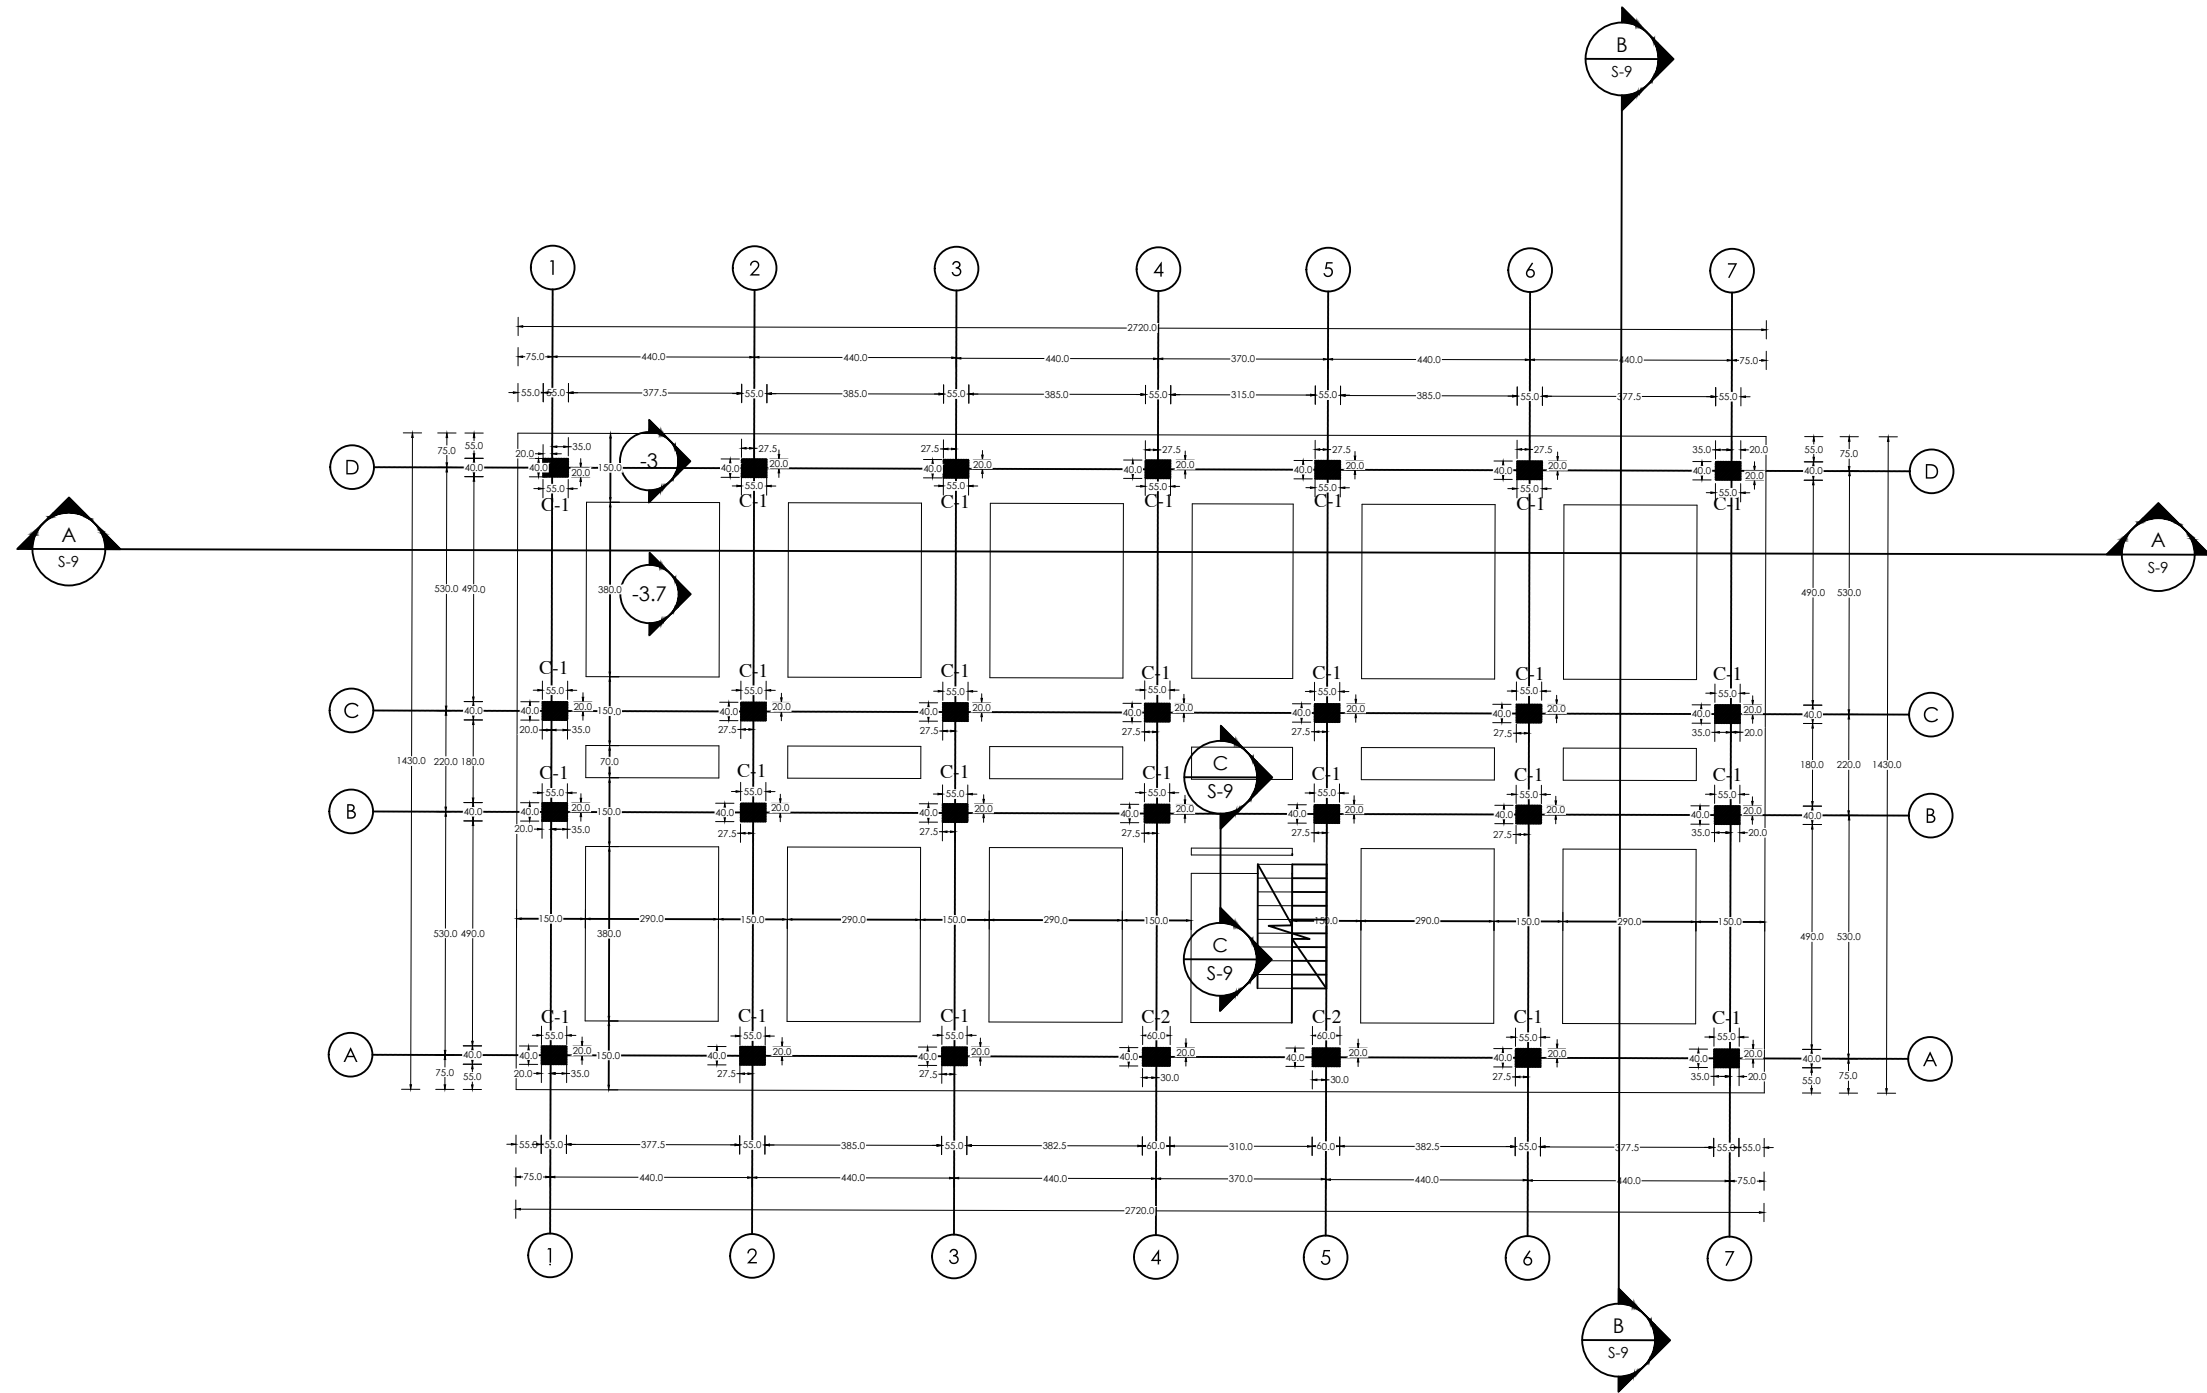

04 | REF. | SCALE: 1:100

Foundation PLAN
and Column Layout

NOTES:
1-FOUNDATION DEPTH = 60cm
2-Fc = 4000 psi
3-Fy = 60000 psi