


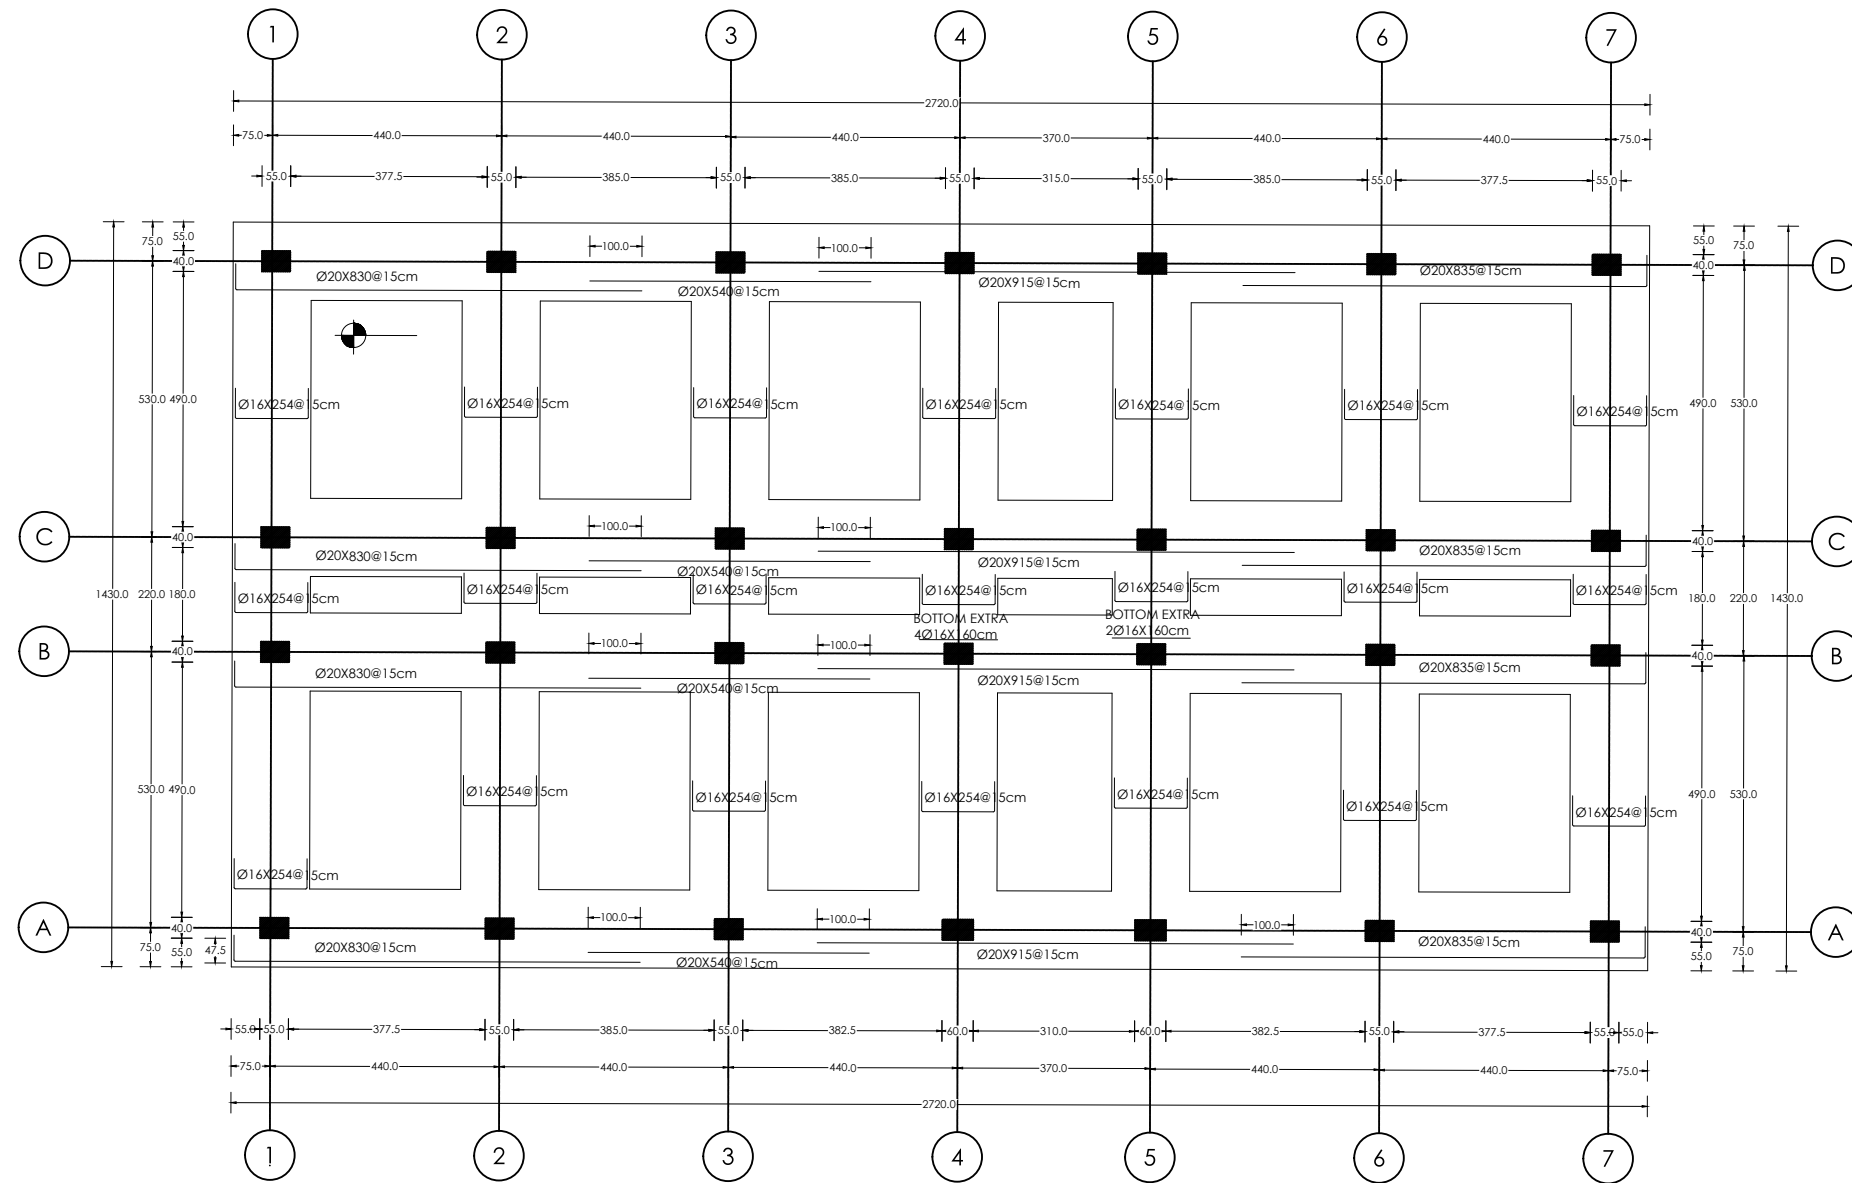

05 Foundation Bottom
Reinforcement @ X Direction
S-05 REF. SCALE: 1:100

NOTES:
1-FOUNDATION DEPTH = 60cm
2-Fc = 4000 psi
3-Fy = 60000 psi