


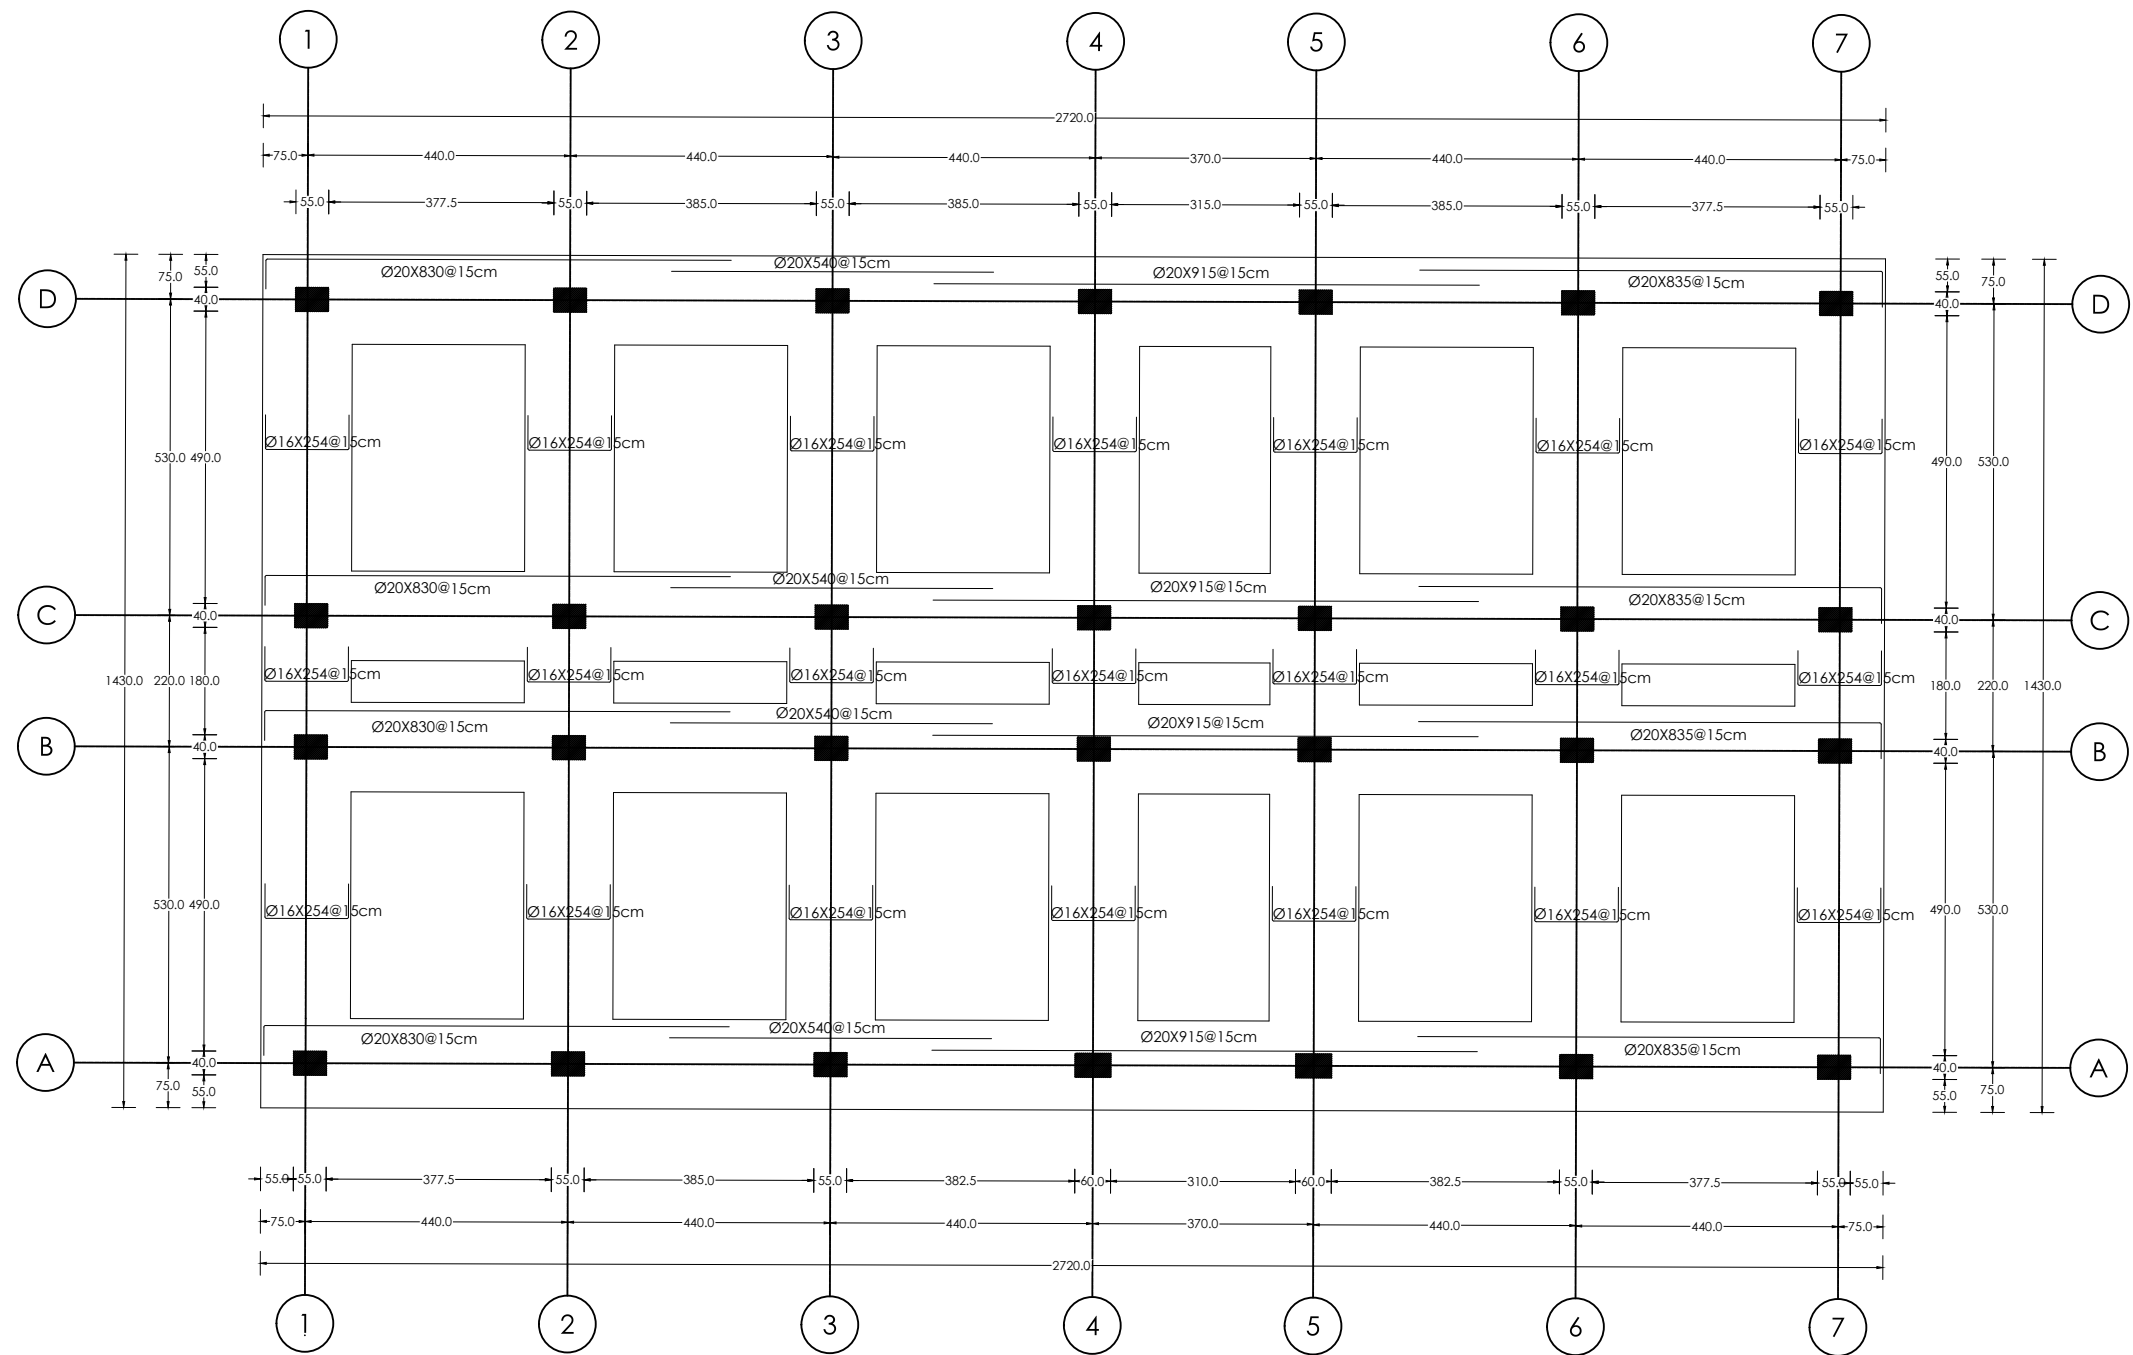

06 Foundation Top
Reinforcement @ X Direction
S-06 REF. SCALE: 1:100

NOTES:
1-FOUNDATION DEPTH =60cm
2-Fc = 4000 psi
3-Fy = 60000 psi