


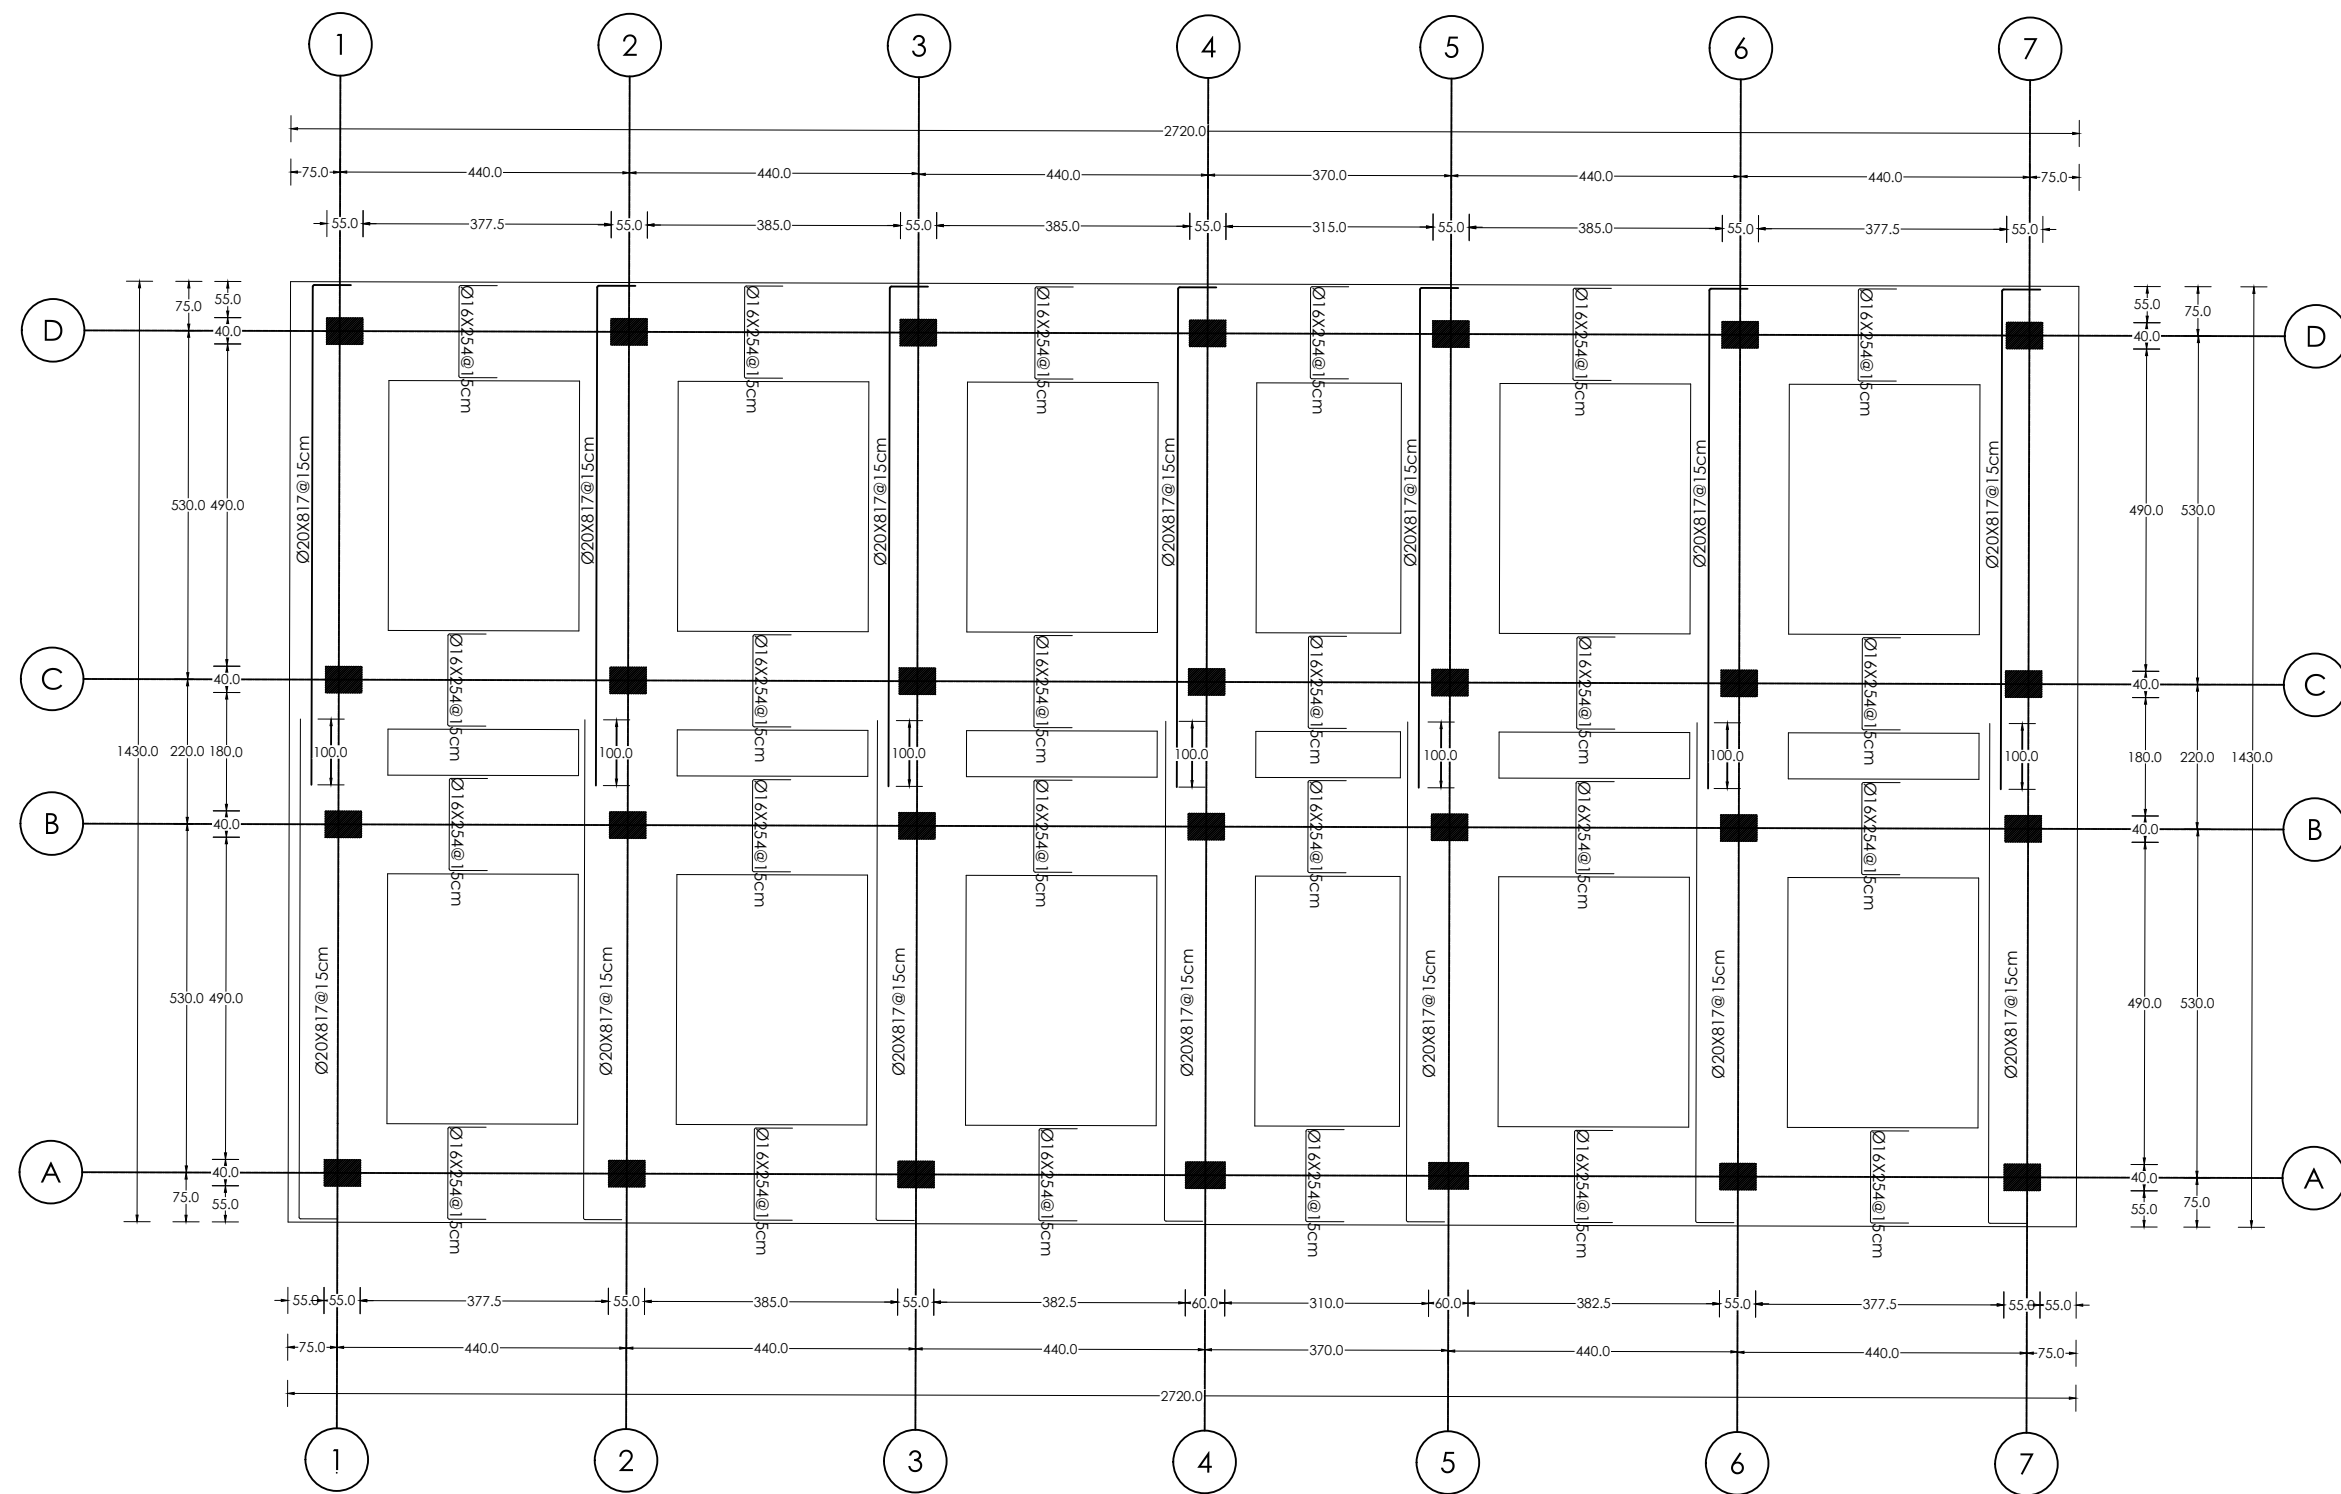

NOTES:
1-FOUNDATION DEPTH =60cm
2-Fc = 4000 psi
3-Fy = 60000 psi